


Согласовано

Взам. инв. №

Подп. и дата

Инв. № подл.

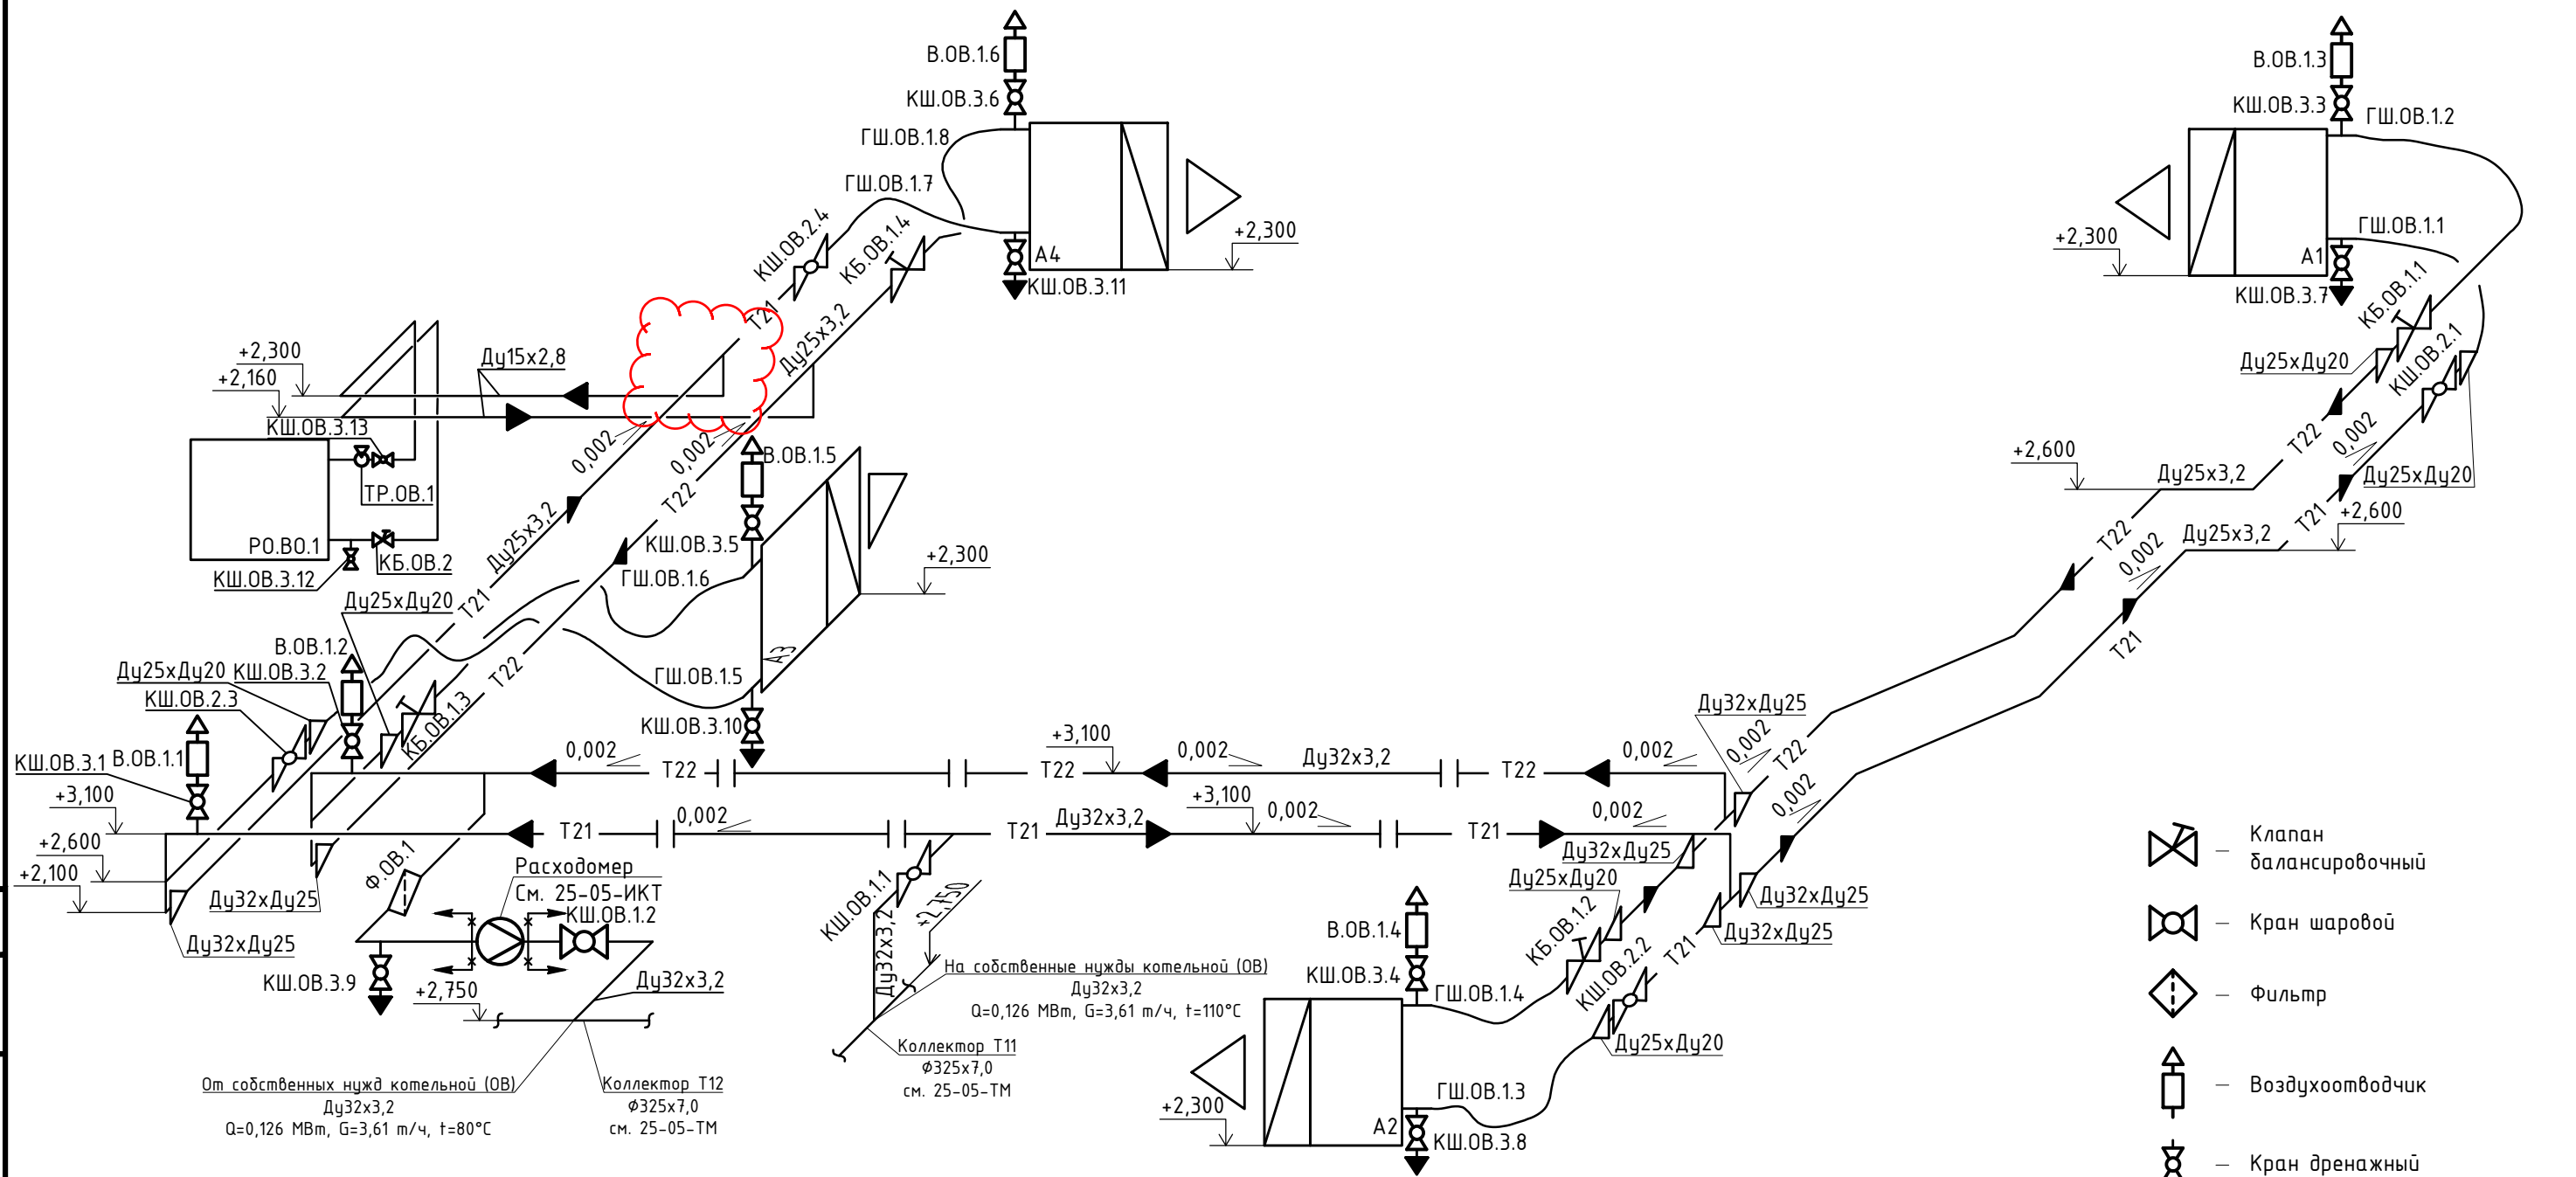


- Клапан балансировочный
- Кран шаровый
- Фильтр
- Воздухоотводчик
- Кран дренажный
- Переход
- Направление движения среды
- Т21 — — Трубопровод подающий
- Т22 — — Трубопровод обратный

Поз. Обозн	Наименование	Кол	Примечание
A1-A4	Воздушно отопительный агрегат ВС-2245, ф. Греерс	4	3 раб. 1 рез.
Ф.ОВ1	Фильтр сетчатый муфтовый	1	Ду32, Ру2,0
ТР.ОВ.1	Терморегулятор радиаторный	1	Ду15, Ру1,6
КШ.ОВ1.1...1.2	Кран шаровый муфтовый	2	Ду32, Ру2,5
КШ.ОВ2.1...2.4	Кран шаровый муфтовый	4	Ду25, Ру4,0
КШ.ОВ3.1...3.13	Кран шаровый муфтовый	13	Ду15, Ру4,0
КБ.ОВ1.1...1.4	Клапан балансировочный муфтовый	4	Ду20, Ру1,6
КБ.ОВ.2	Клапан балансировочный муфтовый	1	Ду15, Ру1,6
В.ОВ1.1...1.6	Воздухоотводчик автоматический	6	Ду15, Ру1,4
ГШ.ОВ1.1...1.8	Гибкий шланг для горячей воды	8	Ду20
Р.О.В.1	Радиатор STOUT BRAVO 500	1	4секц, N=0.7 кВт

						25-05-ОВ			
Изм.	Кол.уч.	Лист	N.док.	Подпись	Дата				
Разраб.						Блочно-модульная водогрейная котельная заводской марки КМ-16 ВГ	Стадия	Лист	Листов
Проверил							Р	3	
						Схема системы отопления	ЭНЕРГО РОСТ СТРОЙ		
Н.контр.									
ГИП									

Схема системы вентиляции

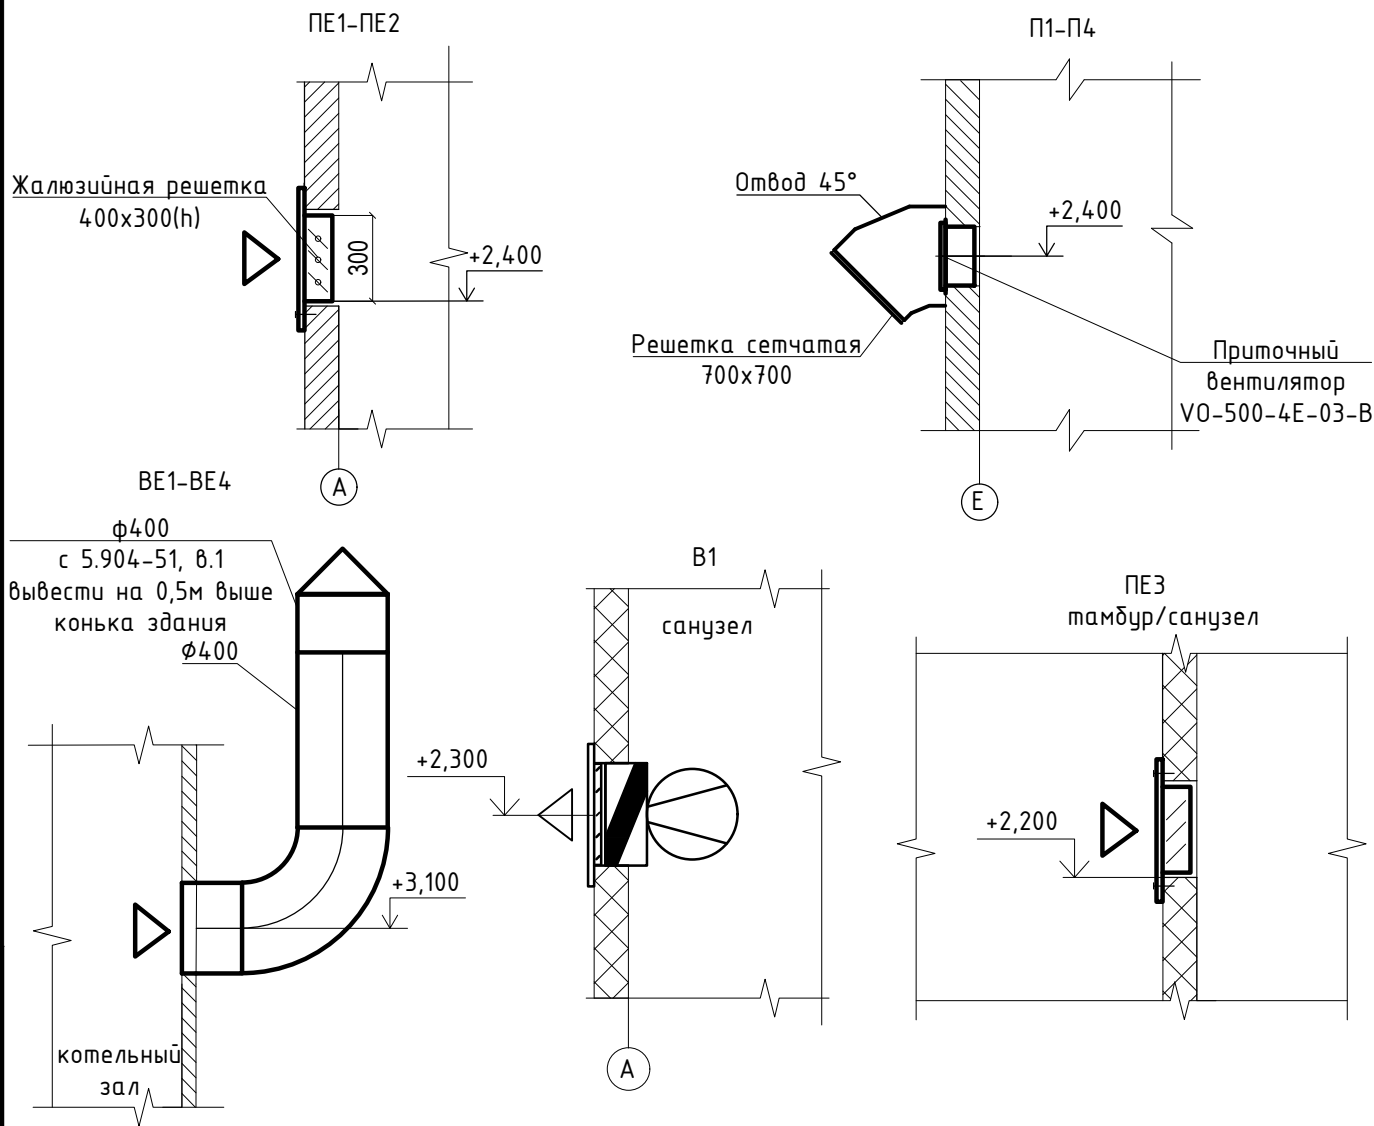

Поз.	Наименование	Кол	Примечание
ПЕ1-ПЕ2	Жалюзийная решетка РН RAL7004 300x400, ф. Nevatом	2	
П1-П4	Вентилятор осевой VO-500-4E-03-B с регулятором скорости, ф. Nevatом	4	
	Решетка сетчатая 700x700мм, РЭД-СРН-св, 700x700, RAL7004, ф. Рэдвент	4	
BE1-BE4	Дефлектор-400-оц-ф, ф. Nevatом	4	
В1	Вытяжной вентилятор SLIM 4C, решетка РНК-100	1	
ПЕЗ	Жалюзийная решетка РН 200x200	1	

25-05-0B

Изм.	Кол.уч.	Лист	И.док.	Подпись	Дата	Блочно-модульная водогрейная котельная заводской марки КМ-16 ВГЖ		
Разраб.								
Проверил						Схема системы вентиляции		
Н.контр.								
ГИП						 ЭНЕРГО РОСТ СТРОЙ		