


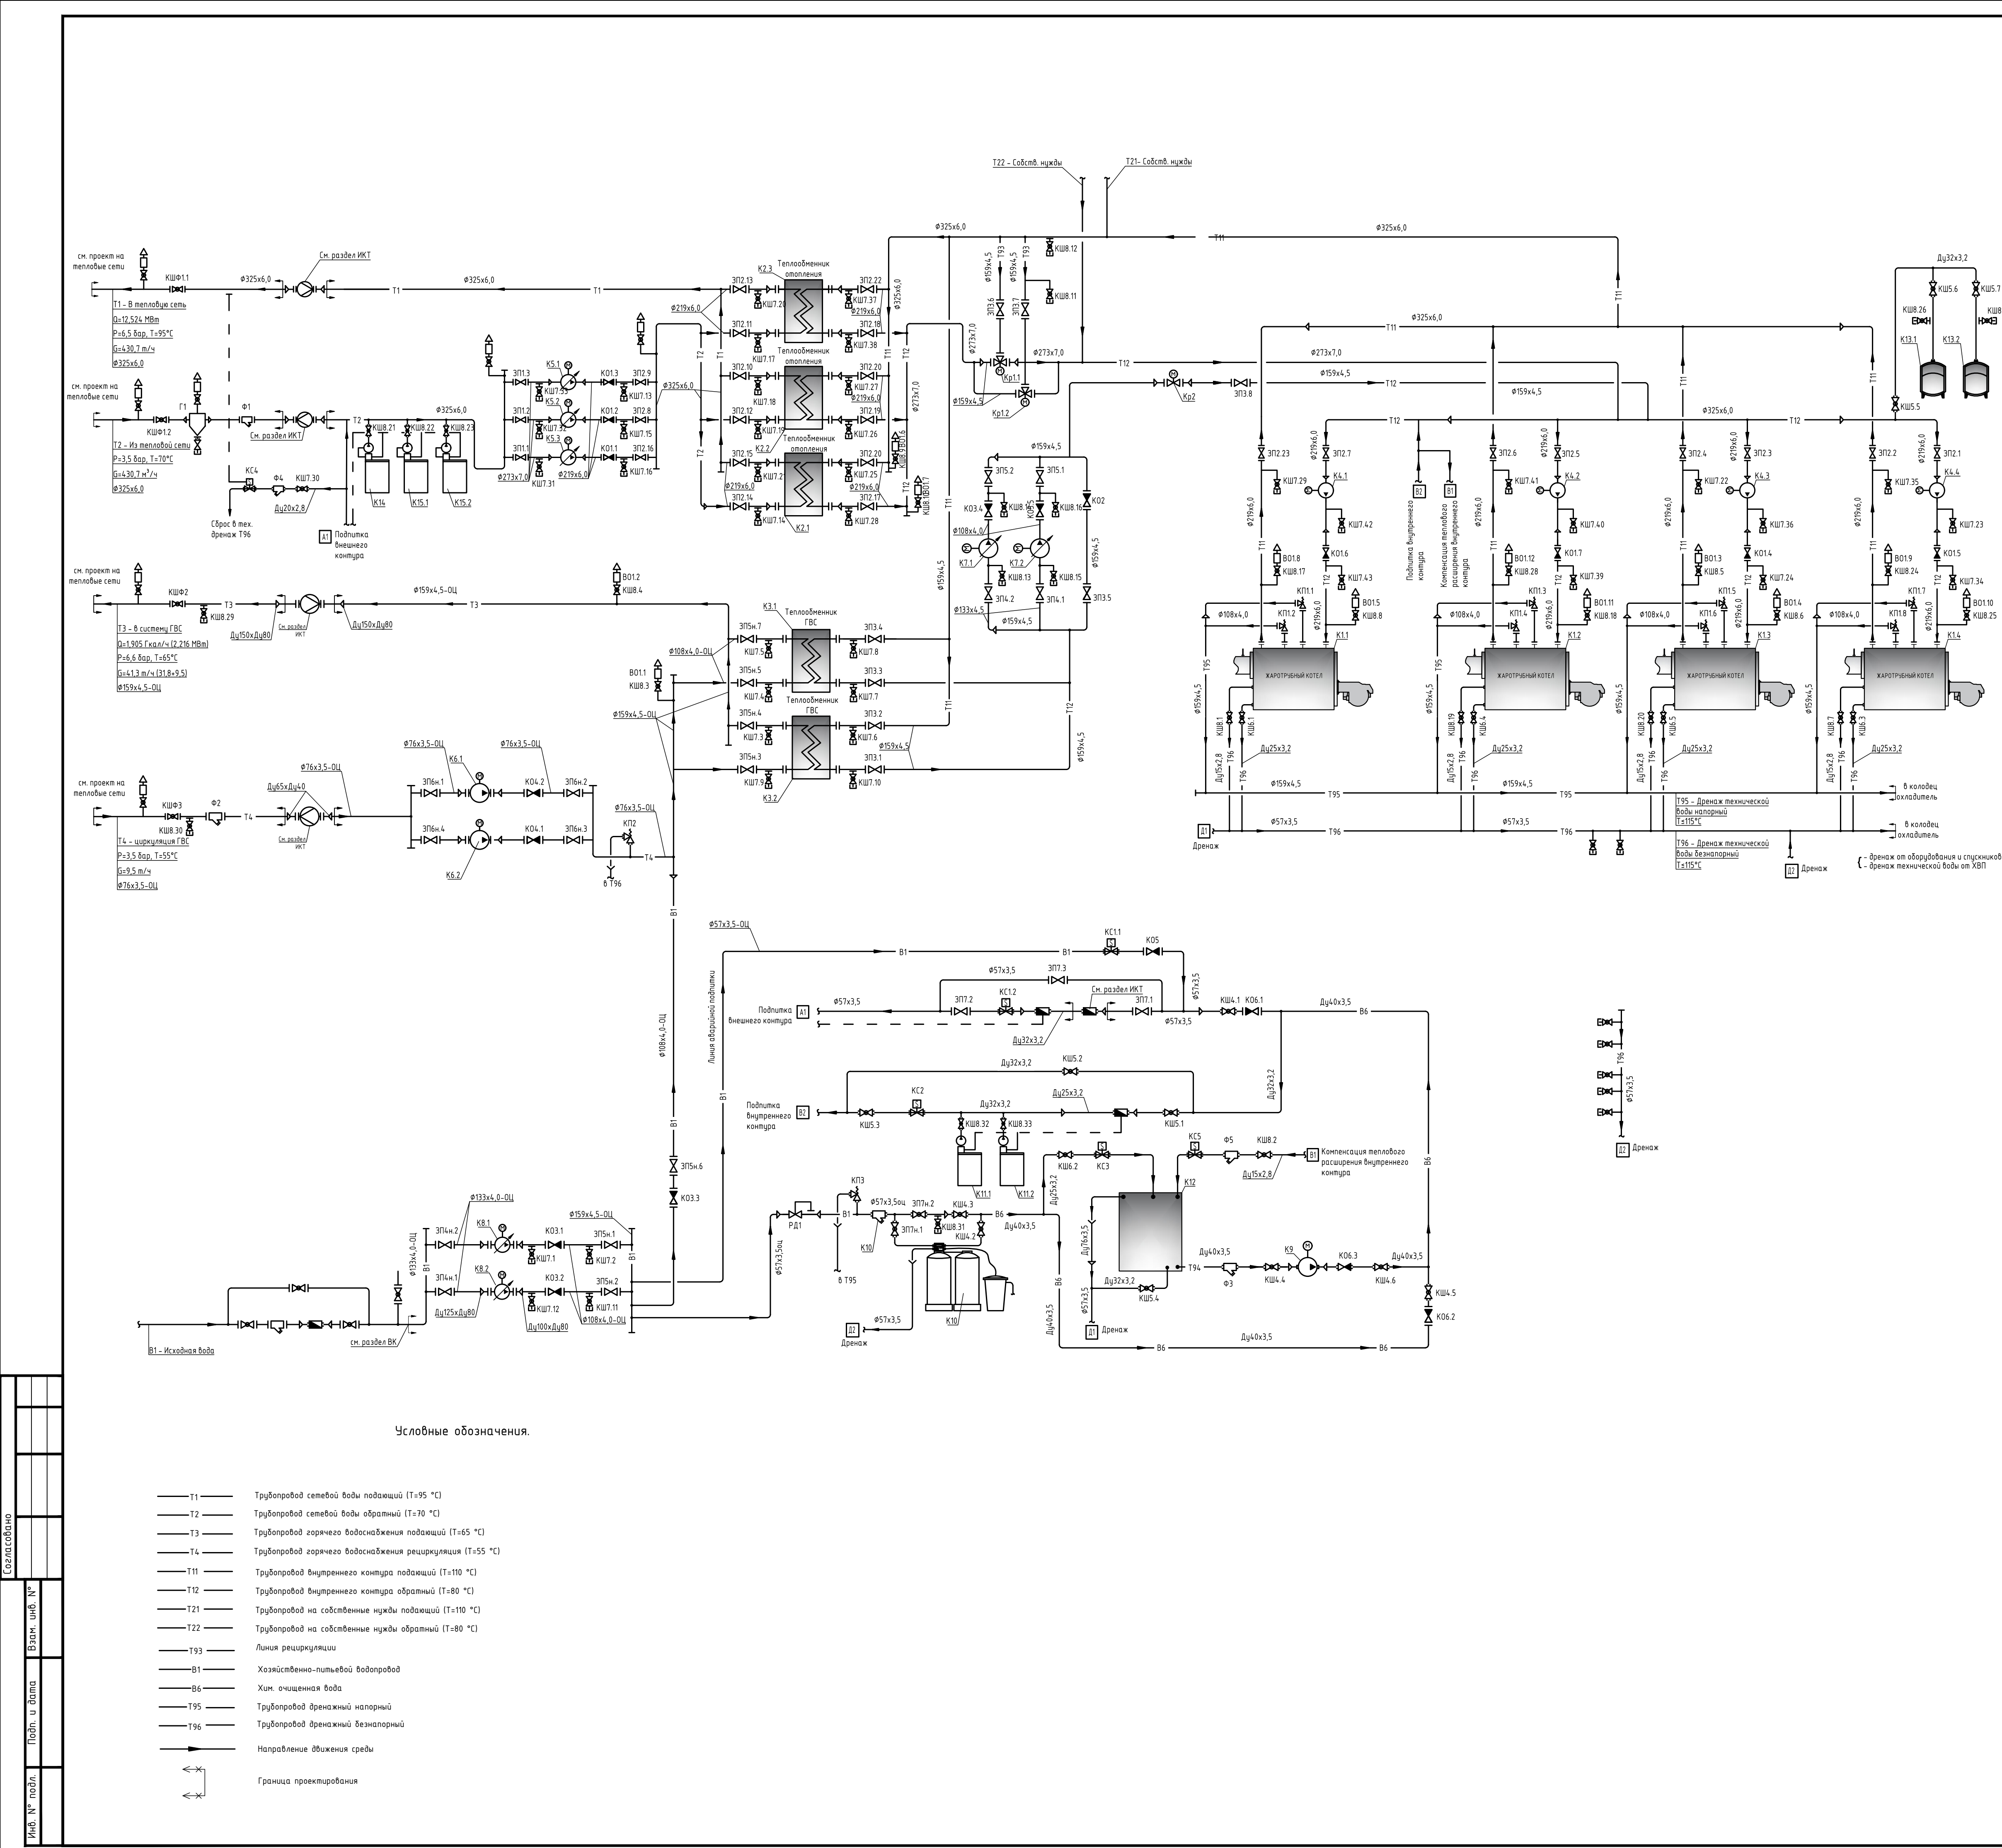

Поз.	Наименование	Кол.	Примечание
K11-K14	Котел водогрейный двухходовой Дорогобуж-4000 КВ-ГМ-4, 0-115Н, ф. 000 «Дорогобужкомпаш»	4	Q=4,0 МВт; 11/72-110/80°С; P _{рег} =6,0 бар; T _{мин} =15°С
K2.1-K2.3	Подогреватель системы отопления, пластинчатый HNH41 Расчет w102218002	3	Q=5,384 Гкал/ч (6,262 МВт); 2 раб, 1 резервный
K3.1-K3.2	Подогреватель системы ГВС, пластинчатый HNH41 Расчет w102218005	2	Q=1905 Гкал/ч (2,216 МВт); 1 раб, 1 резервный
K4.1-K4.5	Насос циркуляции котла NIS150-125-200G/5.5 ф. CNP	5	G=118,5 м³/ч; H=7 м; P=5,5 кВт; 4-рабочих, 1-сухой резерв
K5.1-K5.3	Насос сетевой воды TD2000-53/4 ф. CNP	3	G=274,0 м³/ч; H=52,5 м; P=75 кВт; 2-рабочих, 1 резервный
K6.1-K6.2	Насос циркуляции ГВС внешний контур CHL12-40, ф. CNP	2	G=9,7 м³/ч; H=39 м; P=2,4 кВт; 1-рабочий, 1 резервный
K7.1-K7.2	Насос циркуляции ГВС внутренний контур с ЧРП LLS80-5-15, ф. CNP	2	G=4,8 м³/ч; H=3 м; P=1,5 кВт; 2 рабочих
K8.1-K8.2	Насос исходной воды CDM42-4 с ЧРП, ф. CNP	2	G=4,0 м³/ч; H=65 м; P=15,0 кВт; 1-рабочий, 1-резервный
K9	Насос подпиточной воды CDM3-7, ф. CNP	1	G=2,5 м³/ч; H=4,4 м; P=0,75 кВт;
K10	Автоматическая установка умягчения непрерывного действия	1	G=2,5 м³/ч;
K11	Комплекс дозирования реагента	2	
K12	Бак запаса подпиточной воды V=4 м³, стальной	1	V=4000 л
K13	Мембранный расширительный бак Wester WRV 1000	2	V=1000 л
K14	Комплекс дозирования реагента	1	
K15.1-K15.2	Комплекс дозирования реагента	2	
Г1	Грязевик ТС-568.00.000-06	1	Ду350, Ру1,6, б=485м/ч
Ф1	Фильтр сетчатый фланцевый	1	Ду300, Ру1,6
Ф2	Фильтр сетчатый фланцевый	1	Ду65, Ру1,6
Ф3	Фильтр сетчатый муфтовый	1	Ду40, Ру1,6
Ф4	Фильтр сетчатый муфтовый	1	Ду20, Ру1,6
Ф5	Фильтр сетчатый муфтовый	1	Ду15, Ру1,6
KP1.1-KP1.2	Клапан регулирующий ф. КПСР 3-х ходовой TF 150 3VGS-HS.14 с приводом с трехпозиционным управлением и аналоговой обратной связью TW 3000 XD 220-S.14	2	Ду150, Ру1,6, Kvs350
KP2	Регулирующий двухходовой клапан КПСР ф. КПСР со скоростным приводом с трехпозиционным управлением и аналоговой обратной связью TW 3000 XD 220-S.12	1	Ду100, Ру1,6, Kvs160
KП1	Клапан предохранительный Т7С28мж, Рн.ср.=6,0бар	8	Ду80/100, Ру1,6
KП2	Клапан предохранительный VT.1831N.06 ф. Valtec, Рн.ср.=8,0 бар	1	Ду25, Ру1,6
KП3	Клапан предохранительный, Рн.ср.=6,0 бар VT.1831 ф. Valtec	1	Ду25, Ру1,6
РД1	Регулятор давления типа "после себя" VT.086.NH ф. Valtec	1	Ду25, Ру1,6
КС1	Клапан электромагнитный н/з СК-11 Росма	2	Ду50, Ру1,6
КС2	Клапан электромагнитный н/з СК-11 Росма	1	Ду32, Ру1,6
КС3	Клапан электромагнитный н/з СК-11 Росма	1	Ду25, Ру1,6
КС4	Клапан электромагнитный н/з СК-11 Росма	1	Ду20, Ру1,6
КС5	Клапан электромагнитный н/з СК-11 Росма	1	Ду15, Ру1,6
ЗП1	Затвор поворотный с редуктором, диск из чугуна ЗДМ ф. Ридан	3	Ду250, Ру1,6
ЗП2	Затвор поворотный с редуктором, диск из чугуна ЗДМ ф. Ридан	23	Ду200, Ру1,6
ЗП3	Затвор поворотный с рукояткой, диск из чугуна ЗДМ ф. Ридан	8	Ду150, Ру1,6
ЗП4	Затвор поворотный с рукояткой, диск из чугуна ЗДМ ф. Ридан	2	Ду125, Ру1,6
ЗП4н	Затвор поворотный с рукояткой, диск из нерж. стали ЗДМ ф. Ридан	2	Ду125, Ру1,6
ЗП5	Затвор поворотный с рукояткой, диск из чугуна ЗДМ ф. Ридан	2	Ду100, Ру1,6
ЗП5н	Затвор поворотный с рукояткой, диск из нерж. стали ЗДМ ф. Ридан	7	Ду100, Ру1,6
ЗП6н	Затвор поворотный с рукояткой, диск из нерж. стали ЗДМ ф. Ридан	4	Ду65, Ру1,6
ЗП7	Затвор поворотный с рукояткой, диск из чугуна ЗДМ ф. Ридан	3	Ду50, Ру1,6
ЗП7н	Затвор поворотный с рукояткой, диск из нерж. стали ЗДМ ф. Ридан	2	Ду50, Ру1,6
КШФ1	Кран шаровый фланцевый, стандартнопроходной, с редуктором	2	Ду300, Ру1,6
КШФ2	Кран шаровый фланцевый, стандартнопроходной, с рукояткой	1	Ду150, Ру1,6
КШФ3	Кран шаровый фланцевый, стандартнопроходной, с рукояткой	1	Ду65, Ру1,6
КШ4	Кран шаровый муфтовый ВР/ВР LD Pride	6	Ду40, Ру1,6
КШ5	Кран шаровый муфтовый ВР/ВР LD Pride	7	Ду32, Ру1,6
КШ6	Кран шаровый муфтовый ВР/ВР LD Pride	7	Ду25, Ру1,6
КШ7	Кран шаровый муфтовый ВР/ВР LD Pride	43	Ду20, Ру1,6
КШ8	Кран шаровый муфтовый ВР/ВР LD Pride	31	Ду15, Ру1,6
КО1	Клапан обратный межфланцевый, двухстворчатый, диск из нерж. стали ЗОД.01.16.200 ф. Ридан	7	Ду200, Ру1,6
КО2	Клапан обратный межфланцевый, двухстворчатый, диск из нерж. стали ЗОД.01.16.150 ф. Ридан	1	Ду150, Ру1,6
КО3	Клапан обратный межфланцевый, двухстворчатый, диск из нерж. стали ЗОД.01.16.100 ф. Ридан	5	Ду100, Ру1,6
КО4	Клапан обратный межфланцевый, двухстворчатый, диск из нерж. стали ЗОД.01.16.65 ф. Ридан	2	Ду65, Ру1,6
КО5	Клапан обратный межфланцевый, двухстворчатый, диск из нерж. стали ЗОД.01.16.50 ф. Ридан	1	Ду50, Ру1,6
КО6	Клапан обратный муфтовый латунный	3	Ду40, Ру1,6
В01	Воздухоотводчик автоматический R99 HP прямой, ф. Giacomini	12	Ду15; Ру=1,4МПа T _{max} =120°С

25-05-ТМ

Изм.

Кол.ч.

Лист

Н.док

Подпись

Дата

Разраб.

Проверил

Н.контр.

ГИП

Блочно-модульная водогрейная котельная заводской марки КМ-16,0БГ

Стадия

Лист

Листов

Р

2

Тепловая схема котельной

ЭНЕРГО РОСТ СТРОЙ

Формат А1

25/8/2025 6:22:26