


|             |                |            |
|-------------|----------------|------------|
| Инв.№ подл. | Подпись и дата | Взам.инв.№ |
|             |                |            |

|   |                           |
|---|---------------------------|
| Источник питания   |                           |
| Аппарат на вводе<br>(выключатель автоматический или выключатель нагрузки): номер; тип; ток расцепителя или номинальный ток, А |                           |
| Аппарат на линии<br>(выключатель автоматический или предохранитель): номер; тип; ток расцепителя или плавкой вставки, А       |                           |
| Пускатель магнитный (устройство защитного отключения или другие аппараты): номер; тип; номинальный ток, А                     |                           |
| Маркировка -<br>расчетная нагрузка, кВт -<br>коэффициент мощности - расчетный ток, А -длина участка, м                        | Марка, сечение проводника |
| Наименование потребителя,<br>наименование линии                                                                               |                           |
| Установленная мощность, кВт                                                                                                   |                           |
| Расчетный ток, А   |                           |

ВРУ (см. 25-05-3М)

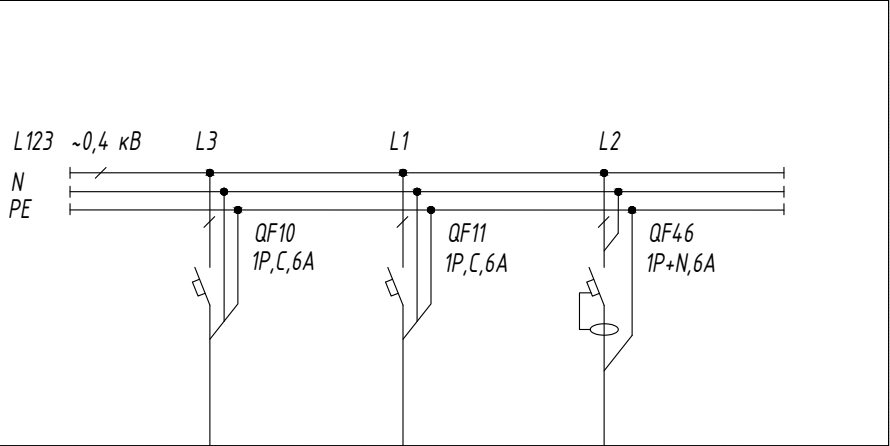

|                                   |                            |                           |
|-----------------------------------|----------------------------|---------------------------|
| Рабочее освещение котельного зала | Ремонтное освещение (12 В) | Рабочее освещение санузла |
| 0,32                              | 0,25                       | 0,04                      |
| 1,53                              | 1,14                       | 0,1                       |

|          |        |      |      |       |      |                                                                 |                              |      |        |
|----------|--------|------|------|-------|------|-----------------------------------------------------------------|------------------------------|------|--------|
|          |        |      |      |       |      | 25-05-30                                                        |                              |      |        |
|          |        |      |      |       |      |                                                                 |                              |      |        |
| Изм.     | Кол.уч | Лист | Ндок | Подп. | Дата |                                                                 |                              |      |        |
| Разраб.  |        |      |      |       |      | Блочно-модульная водогрейная котельная заводской марки КМ-16 ВГ | Стадия                       | Лист | Листов |
| Пров.    |        |      |      |       |      |                                                                 | Р                            | 2    |        |
| Н.контр. |        |      |      |       |      | Рабочее освещение. Схема электрическая однолинейная             | <div>ЭНЕРГО РОСТ СТРОЙ</div> |      |        |
| ГИП      |        |      |      |       |      |                                                                 |                              |      |        |