


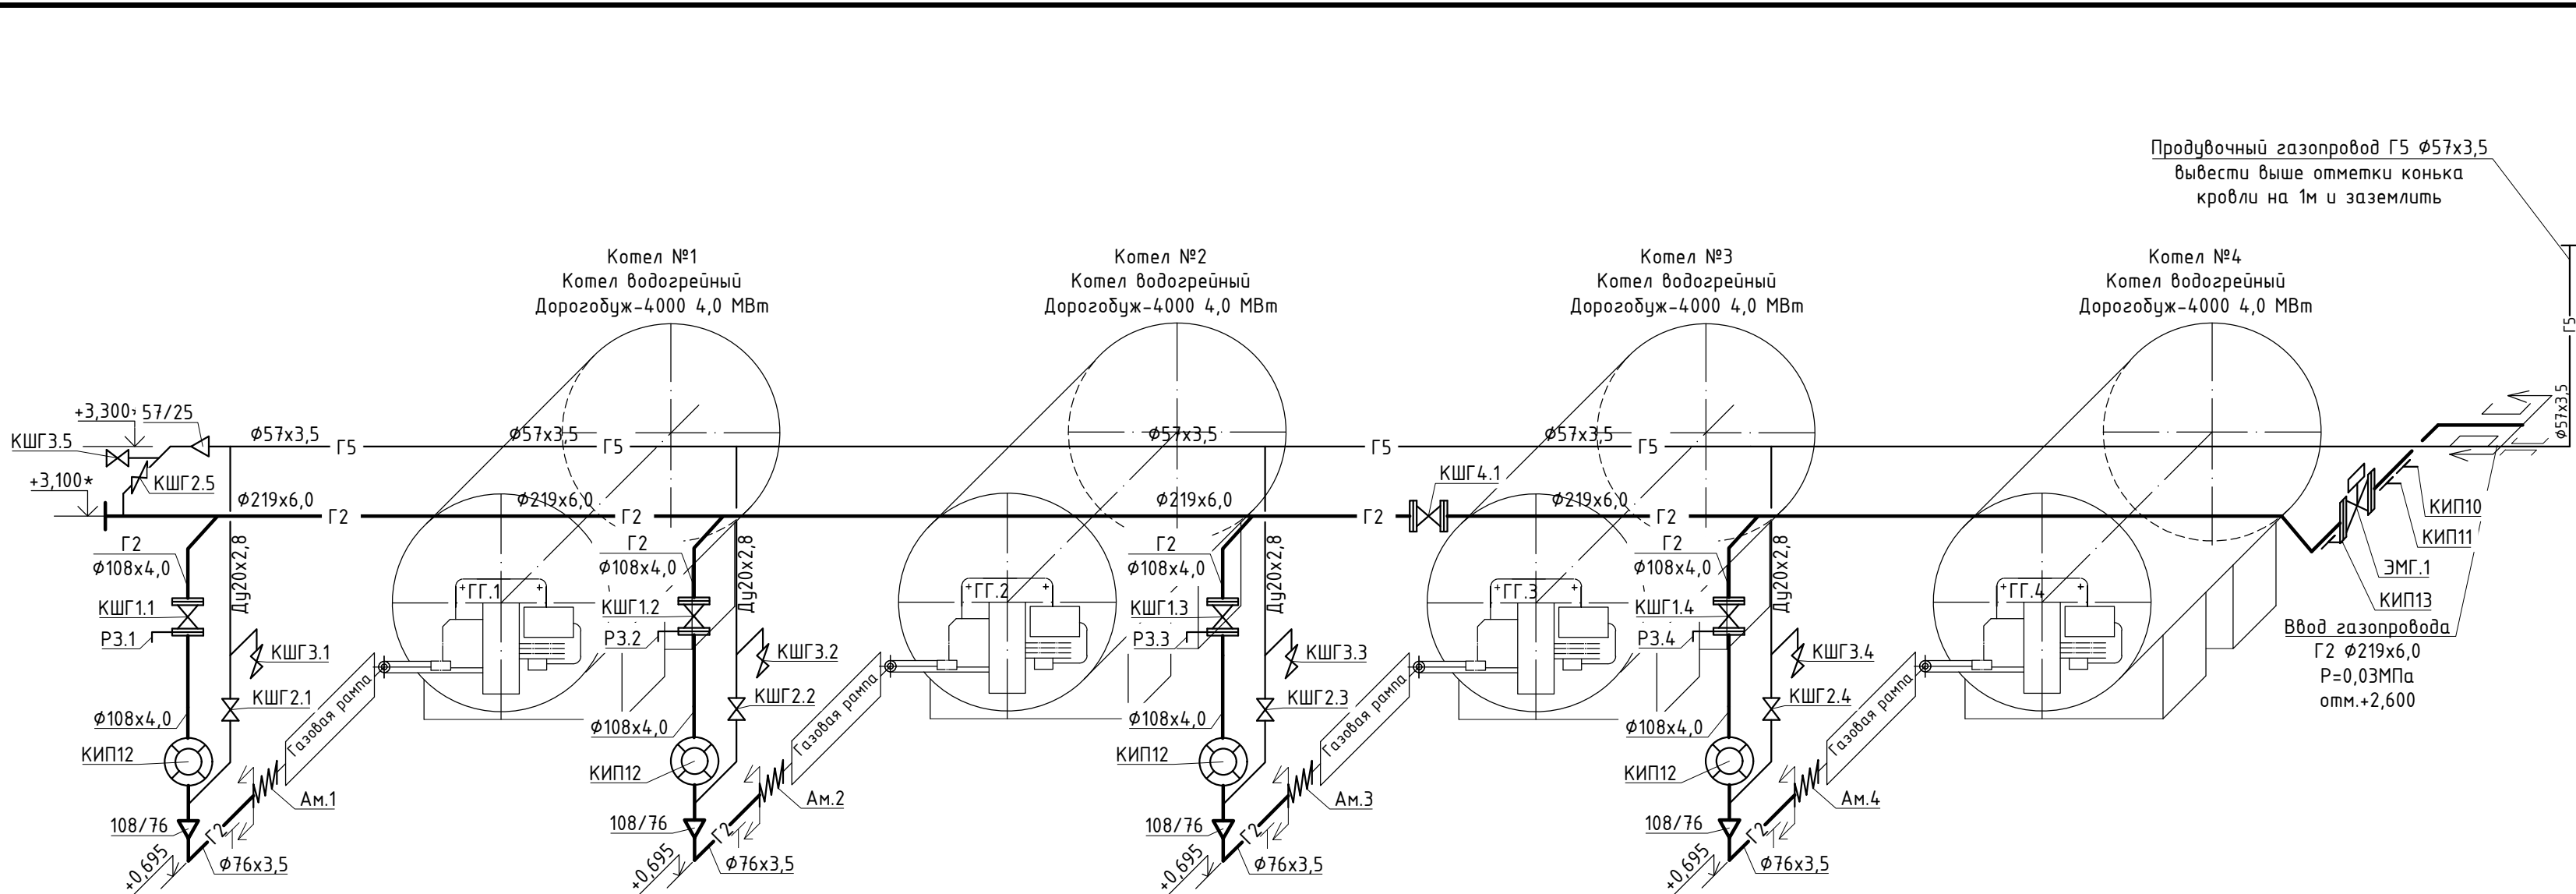

Поз. Обозн	Наименование	Кол	Примечание
ГГ.1...ГГ.4	Горелка газовая TBG 650 ME	4	Baltur
1.1...4.1	Фильтр газовый	1	В комплекте каждой горелки
1.2...4.2	Клапан безопасности	1	
1.3...4.3	Реле min давления газа/контроля герметичности	1	
1.4...4.4	Клапан регулятор расхода газа/стабилизатор давления	1	
1.5...4.5	Реле max давления газа	1	
Ам.1...Ам.4	Антивибрационная муфта Ду65	1	
ЭМГ.1	Электромагн. клапан ВН8Н-1см фл	1	Ду200; Ру0,1МПа
КШГ1.1...КШГ1.4	Кран шаровой фланцевый LD КШ.Ц.Ф.GAS.100.016.П/П.02	4	Ду100; Ру1,6МПа
РЗ.1...РЗ.4	Ремонтная заглушка	4	Ду100; Ру1,6МПа
КШГ2.1...КШГ2.5	Кран шаровой муфтовый LD КШ.Ц.М.020.040.Н/П.02	5	Ду20; Ру4,0МПа
КШГ3.1...КШГ3.5	Кран шаровой муфтовый LD КШ.Ц.М.015.040.Н/П.02	5	Ду15; Ру4,0МПа
КШГ4.1	Кран шаровой фланцевый LD КШ.Ц.Ф.GAS.200.016.П/П.02	1	Ду200; Ру1,6МПа
Позиции КИПуА:			
КИП10	Кран шаровой 11Б27Пм ду 15 М20х1,5 - G ₂ Штуцер приварной Шц-G1/2-ст.20	1	заложены в АК
КИП11	Бобышка под термометр прямая БП1-М20х1,5-30 ВР	1	заложены в АК
КИП12	Счетчик газовый СГ16МТ-650-Р-2 Ду100; Ру1,6МПа	4	заложены в АК
КИП13	Реле давления газа PS-KIPA-500	1	заложены в АК

- Условные обозначения:
- Г2

Газопровод среднего давления

Г5

Продувочный газопровод

Граница проектирования

Переход

Свеча продувочная

Крепление газопровода


Кран шаровой с ремонтной заглушкой

Электромагнитный клапан

Счетчик газа

Кран шаровой муфтовый

Позиции КИПуА

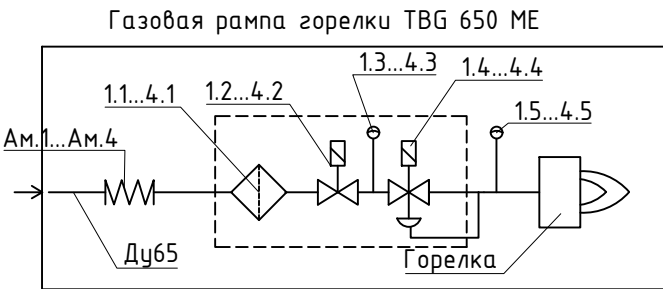

						25-05-ГСВ				
						Строительство БМК (г.о. Сергиев-Посад, г. Хотьково, ул. Ломоносова)				
Изм.	Кол.уч.	Лист	Н.док.	Подпись	Дата	Блочно-модульная водогрейная котельная заводской марки КМ-16,0ВГ		Стадия	Лист	Листов
Разраб.	Козелов			Коз	03.25			Р	2	
Проверил	Дедюхина			Дед	03.25					
						Схема внутреннего газоснабжения		 ЭНЕРГО РОСТ СТРОЙ		
Н.контр.	Дедюхина			Дед	03.25					
ГИП	Куренева			Кур	03.25					