


Согласовано

Взам. инв. №

Подп. и дата


Инв. № подл.

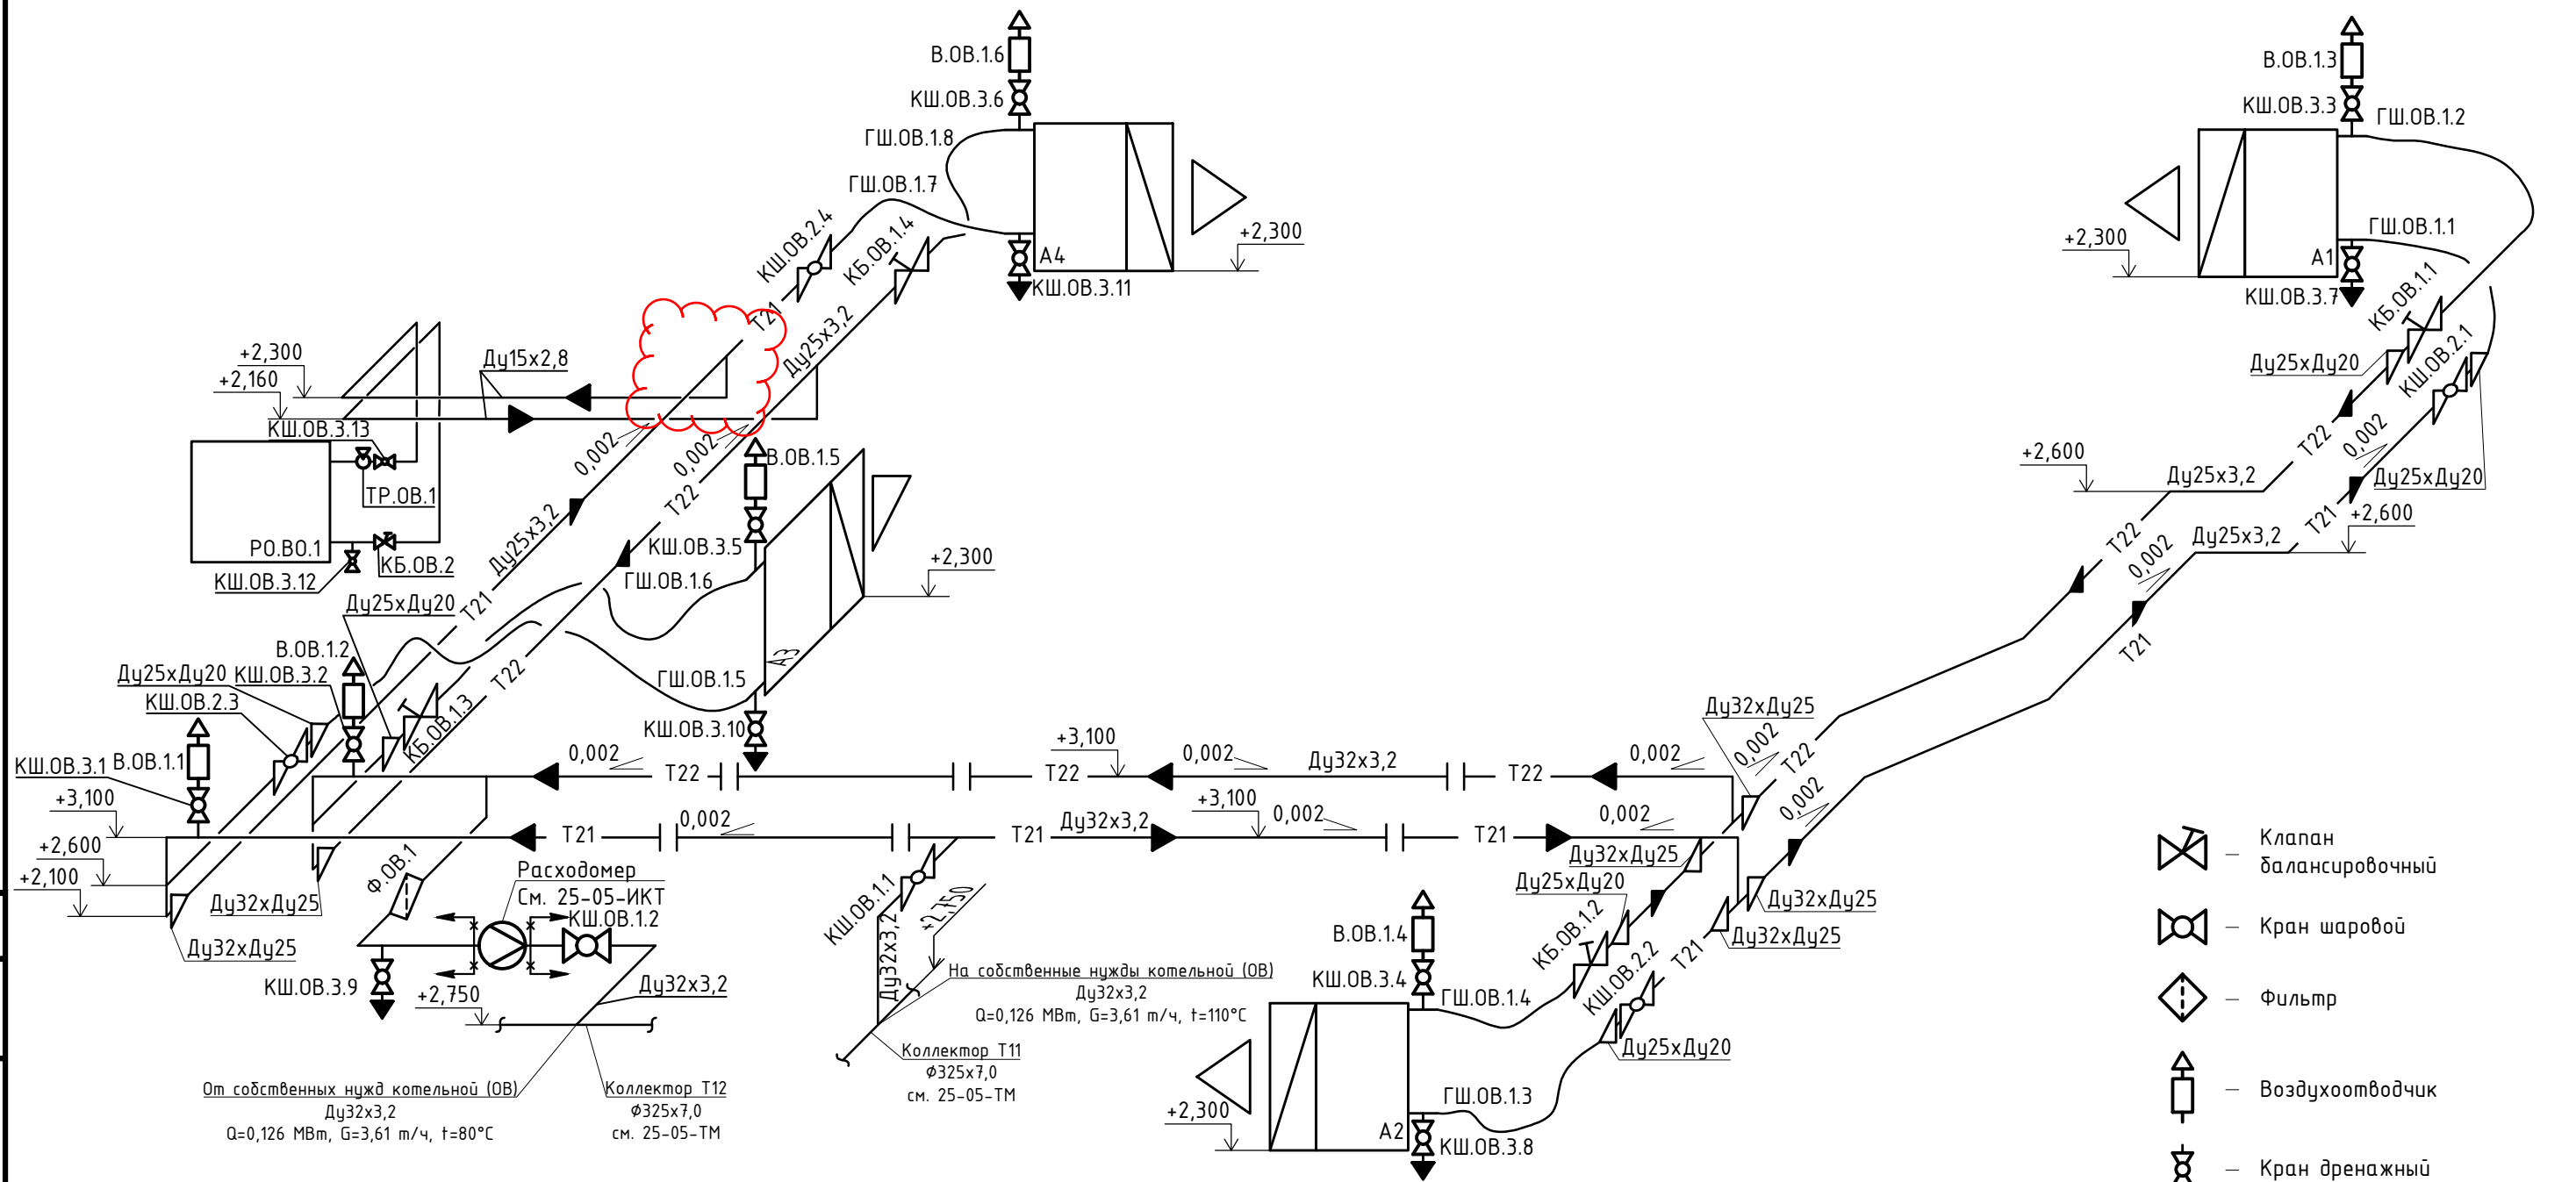

Поз. Обозн	Наименование	Кол	Примечание
A1-A4	Воздушно отопительный агрегат ВС-2245, ф. Греерс	4	3 раб. 1 рез.
Ф.ОБ1	Фильтр сетчатый муфтовый	1	Ду32, Ру2,0
ТР.ОБ.1	Терморегулятор радиаторный	1	Ду15, Ру1,6
КШ.ОБ1.1...1.2	Кран шаровый муфтовый	2	Ду32, Ру2,5
КШ.ОБ2.1...2.4	Кран шаровый муфтовый	4	Ду25, Ру4,0
КШ.ОБ3.1...3.13	Кран шаровый муфтовый	13	Ду15, Ру4,0
КБ.ОБ1.1...1.4	Клапан балансировочный муфтовый	4	Ду20, Ру1,6
КБ.ОБ.2	Клапан балансировочный муфтовый	1	Ду15, Ру1,6
В.ОБ1.1...1.6	Воздухоотводчик автоматический	6	Ду15, Ру1,4
ГШ.ОБ1.1...1.8	Гибкий шланг для горячей воды	8	Ду20
PO.ОБ.1	Радиатор STOUT BRAVO 500	1	4секц, N=0.7 кВт

						25-05-0В			
						Строительство БМК (Сергиев-Посад г.о., г. Хотьково, ул. Ломоносова)			
Изм.	Кол.уч.	Лист	И.док.	Подпись	Дата	Блочно-модульная водогрейная котельная заводской марки КМ-16 ВГ	Стадия	Лист	Листов
Разраб.		Козелов		<i>Козелов</i>	03.25		Р	3	
Проверил		Дедюхина		<i>Дедюхина</i>	03.25				
Н.контр.		Дедюхина		<i>Дедюхина</i>	03.25	Схема системы отопления	 ЭНЕРГО РОСТ СТРОЙ		
ГИП		Полубедов		<i>Полубедов</i>	03.25				

Схема системы вентиляции

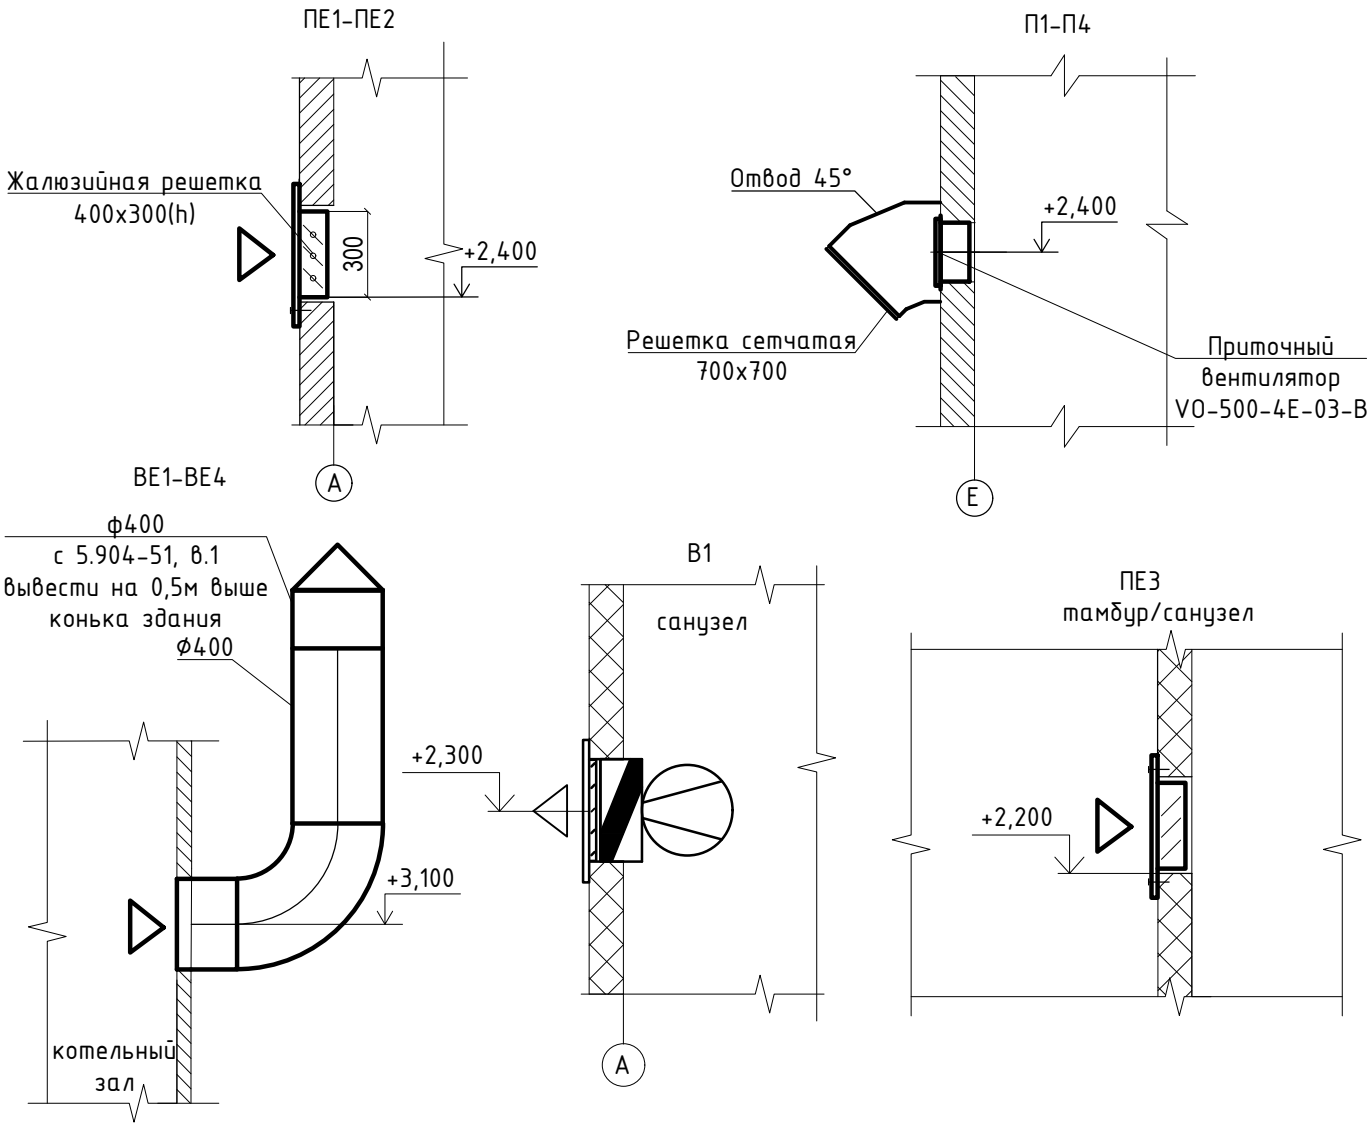

Поз.	Наименование	Кол	Примечание
PE1-PE2	Жалюзийная решетка PH RAL7004 300x400, ф. Nevatом	2	
П1-П4	Вентилятор осевой VO-500-4E-03-B с регулятором скорости, ф. Nevatом	4	
	Решетка сетчатая 700x700мм, РЭД-СРН-св, 700x700, RAL7004, ф. Рэдвент	4	
BE1-BE4	Дефлектор-400-оц-ф, ф. Nevatом	4	
В1	Вытяжной вентилятор SLIM 4С, решетка PHK-100	1	
PE3	Жалюзийная решетка PH 200x200	1	

25-05-0В					
Реконструкция котельной №2 (г.о. Сергиев-Посад, г. Хотьково, ул. Ломоносова, 7а)					
Изм.	Кол.уч.	Лист	Н.док.	Подпись	Дата
Разраб.		Козелов		<i>Kozelov</i>	03.25
Проверил		Дедюхина		<i>Dedyukhina</i>	03.25
Н.контр.		Дедюхина		<i>Dedyukhina</i>	03.25
ГИП		Полубедов		<i>Polubedov</i>	03.25

Блочно-модульная водогрейная котельная заводской марки КМ-16 ВГЖ			Стадия	Лист	Листов
			Р	4	

Схема системы вентиляции			 ЭНЕРГО РОСТ СТРОЙ		
--------------------------	--	--	---	--	--